


ПЛАН КВАРТИРЫ М 1:50

толщина стен 320 мм, размеры в мм

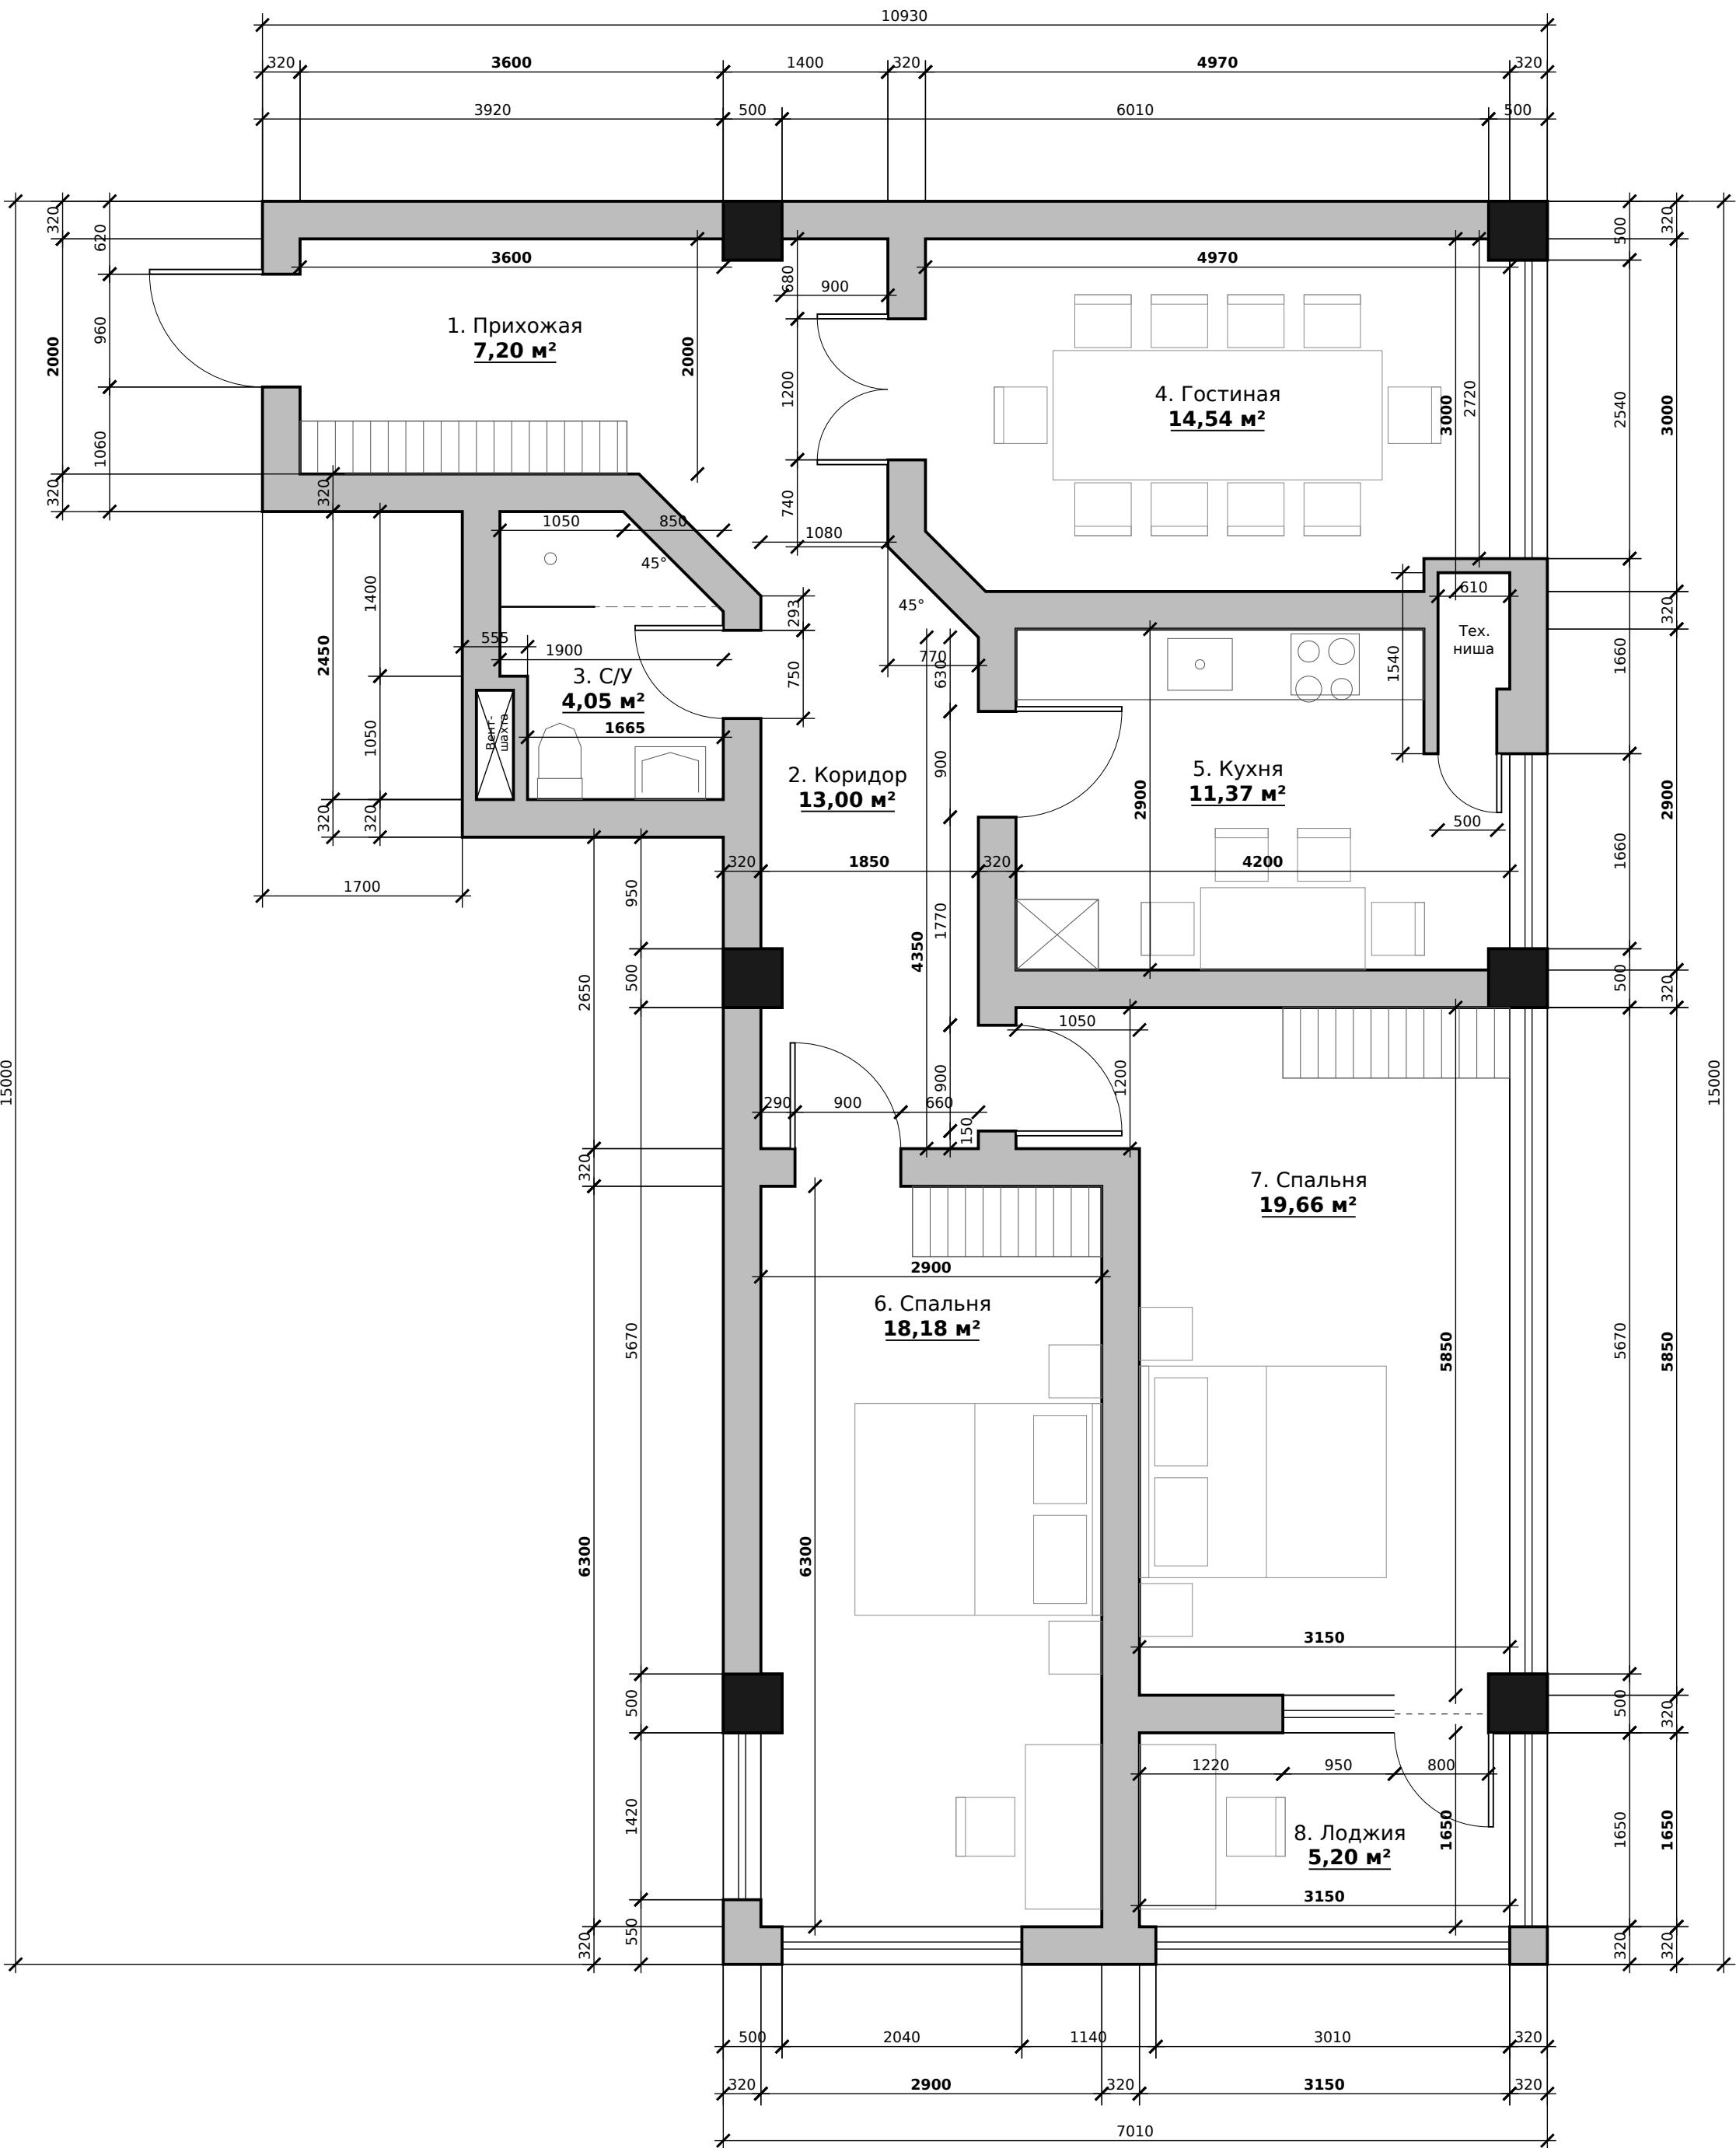

ЭКСПЛИКАЦИЯ ПОМЕЩЕНИЙ

№	Наименование	Room	Площадь, м²
1	Прихожая	Entrance hall	7,20
2	Коридор	Corridor	13,00
3	С/У	Bathroom (WC)	4,05
4	Гостиная	Living room	14,54
5	Кухня	Kitchen	11,37
6	Спальня	Bedroom 1	18,18
7	Спальня	Bedroom 2	19,66
8	Лоджия	Loggia	5,20
Жилая площадь (4, 6, 7)		Living area	52,38
Общая площадь (1-7)		Total area	88,00
Итого с лоджией (1-8)		Total incl. loggia	93,20

ПРИМЕЧАНИЯ

- Все размеры в миллиметрах, площади в м². Масштаб 1:50 — печатать на листе А2 в масштабе 100 % (без подгонки).
- Толщина всех стен 320 мм. Стенки вентиляционные и тех. ниши 120 мм.
- Жирным шрифтом — размеры помещений в чистоте по исходному плану (сохранены без изменений). Остальные размеры получены расчётом или обмером исходного плана с округлением.
- Сечение колонн 500х500 принято условно (в исходном плане не указано); колонны заподлицо с наружной гранью стен.
- Площади подсчитаны по чертежу (в чистоте, за вычетом колонн, без площади проёмов), Площадь тех. ниши 0,88 м² не учтена.
- Мебель показана условно, по исходному плану.
- Контроль масштаба: отрезок 0-5 м на шкале = 100 мм.



УСЛОВНЫЕ ОБОЗНАЧЕНИЯ

- Стена 320 мм
- Колонна 500х500
- Окно / витраж
- Размер по исходному плану

						Квартира: 3 комнаты, лоджия			
						Архитектурные решения			
Изм.	Кол.	Лист	№ док	Подп.	Дата	План квартиры Стены 320 мм	Стадия	Лист	Листов
							Р	1	1
							М 1:50		
							Формат А2		