


ПЛАН КВАРТИРЫ М 1:50

стены 320 мм, справа и снизу — панорамное остекление; размеры в мм

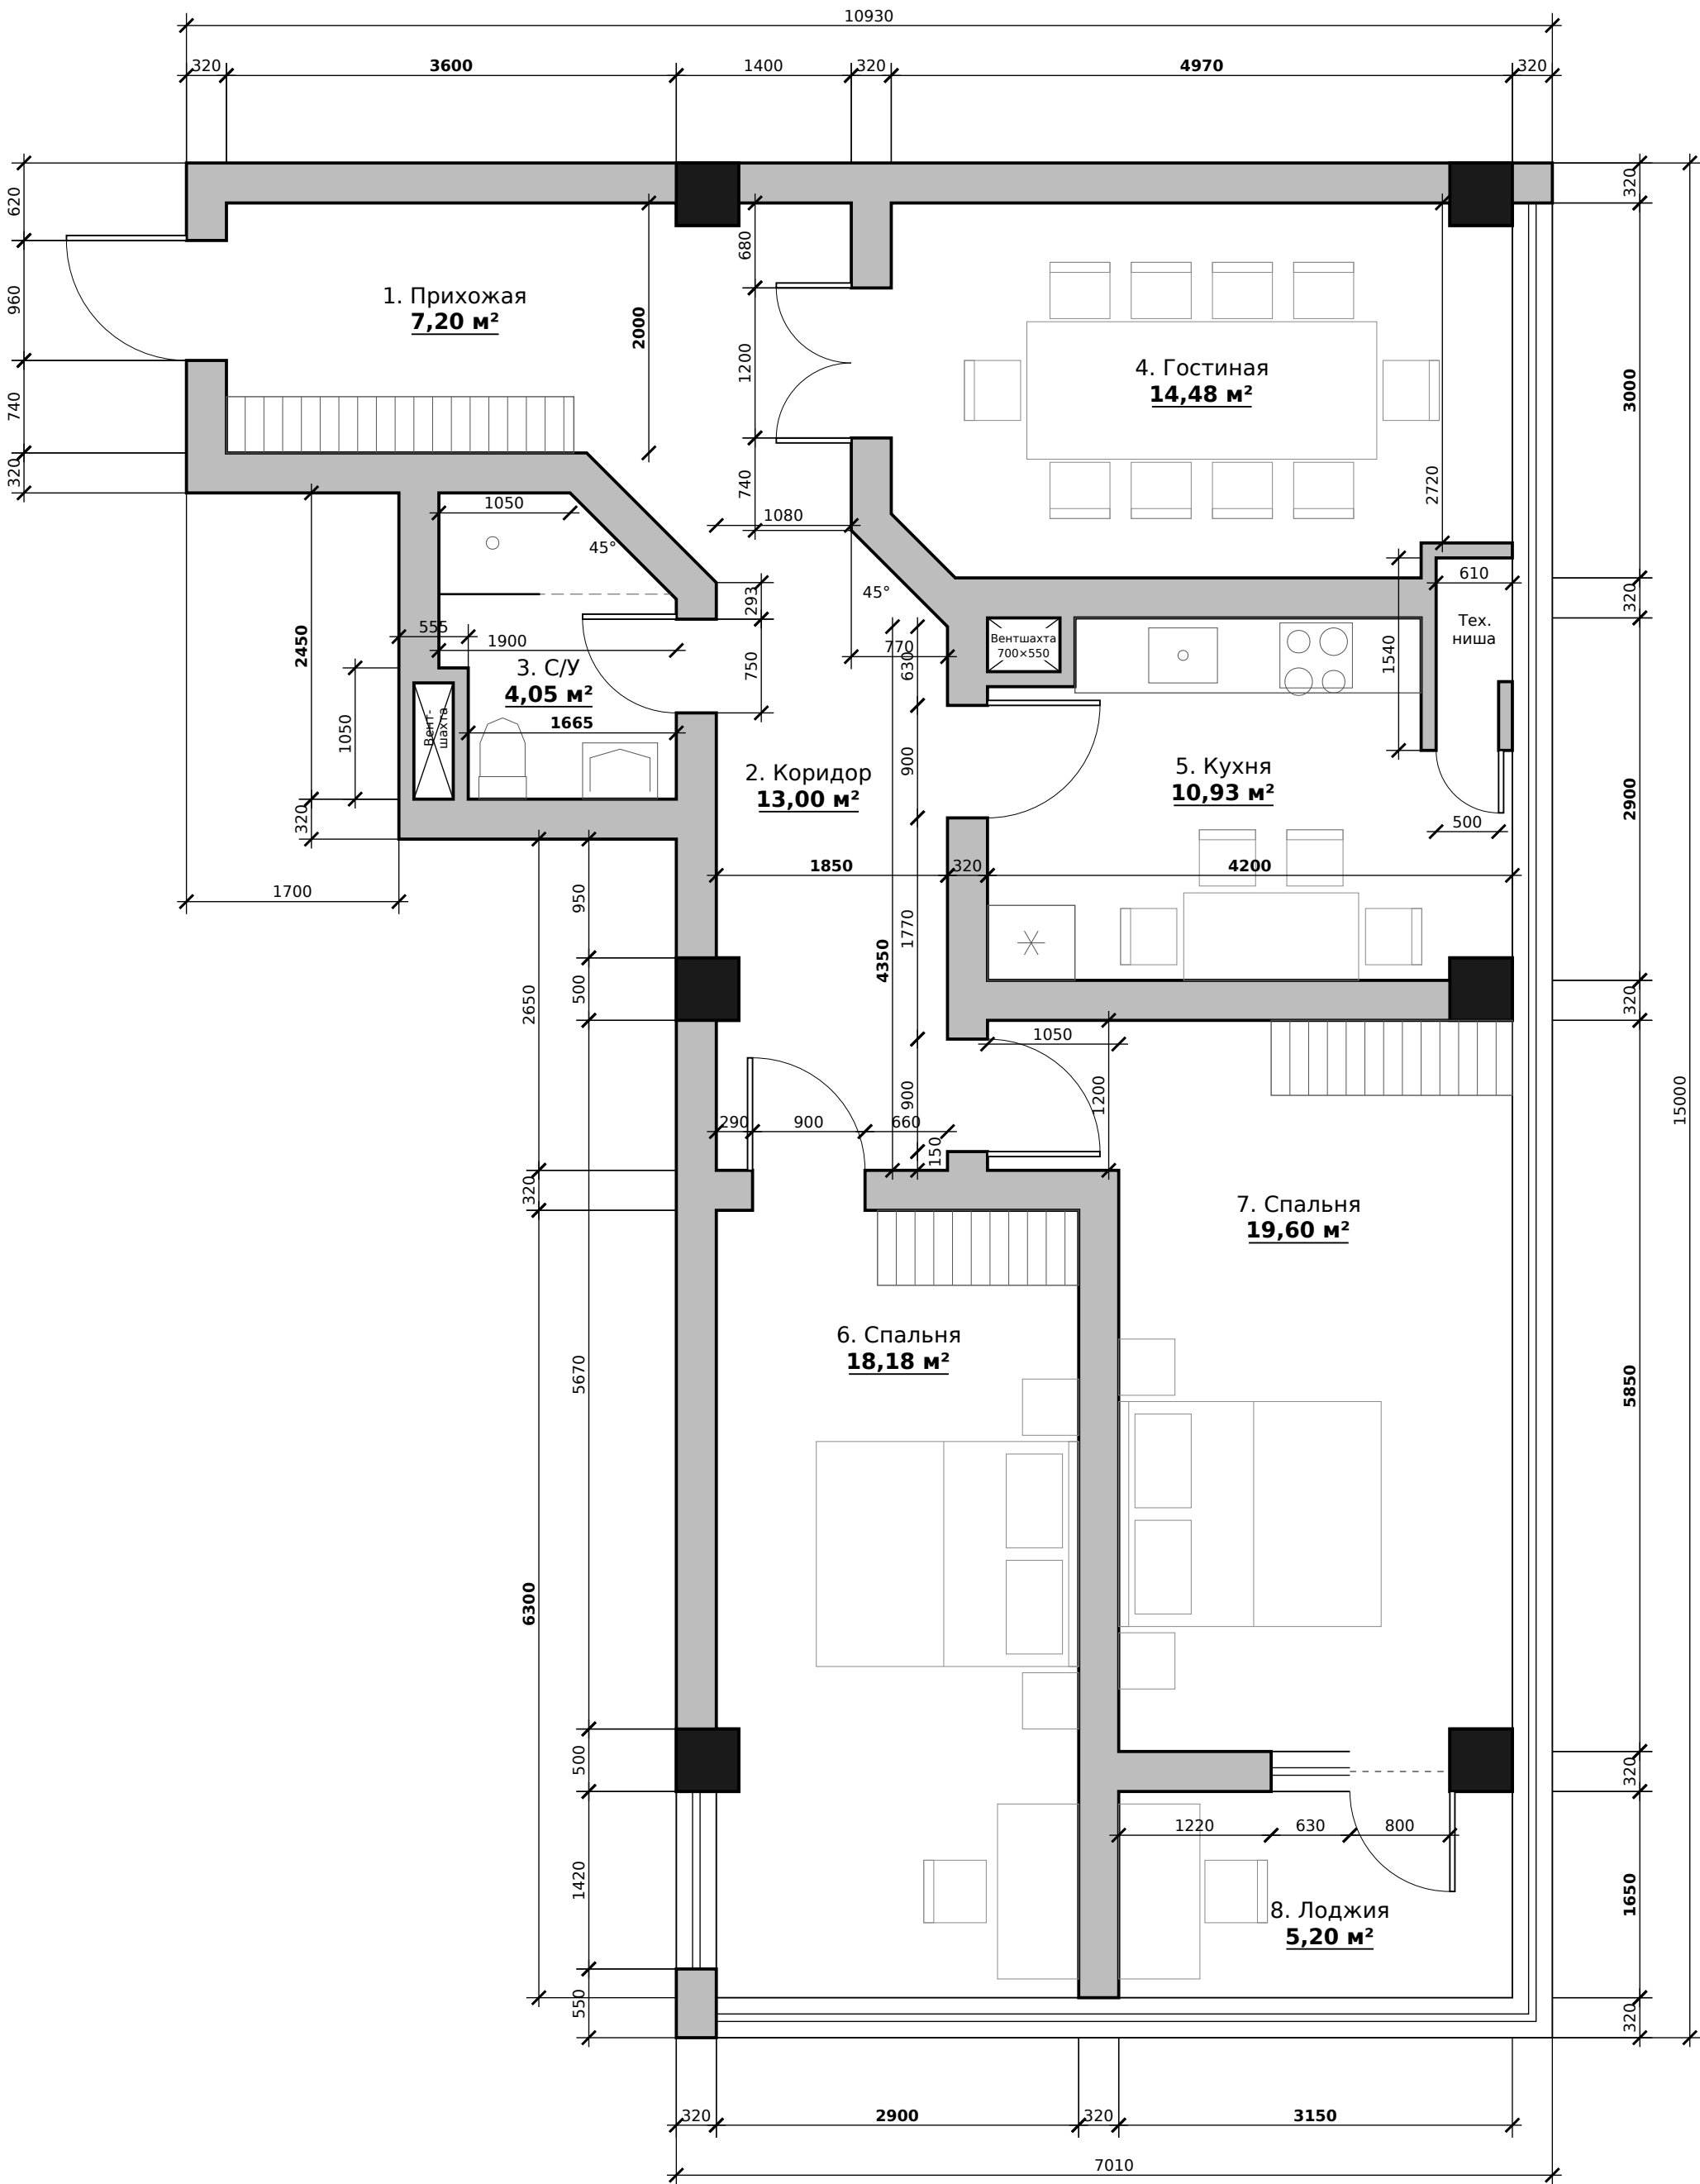

ЭКСПЛИКАЦИЯ ПОМЕЩЕНИЙ

№	Наименование	Room	Площадь, м²
1	Прихожая	Entrance hall	7,20
2	Коридор	Corridor	13,00
3	С/У	Bathroom (WC)	4,05
4	Гостиная	Living room	14,48
5	Кухня	Kitchen	10,93
6	Спальня	Bedroom 1	18,18
7	Спальня	Bedroom 2	19,60
8	Лоджия	Loggia	5,20
Жилая площадь (4, 6, 7)		Living area	52,26
Общая площадь (1-7)		Total area	87,44
Итого с лоджией (1-8)		Total incl. loggia	92,64

ПРИМЕЧАНИЯ

- Все размеры в миллиметрах, площади в м². Масштаб 1:50 — печатать на листе А2 в масштабе 100 % (без подгонки).
- Толщина всех стен 320 мм. Стенки вентшахт и тех. ниши 120 мм.
- Правая и нижняя наружные стороны — сплошное панорамное остекление (витраж) на всю длину, зона 320 мм.
- Жирным шрифтом — размеры помещений в чистоте по исходному плану (сохранены без изменений). Остальные размеры получены расчётом или обмером исходного плана с округлением. Каждый размер указан один раз.
- Колонны 500×500 приняты условно (в исходном плане не указаны): у стен — заподлицо с наружной гранью, у витража — внутри помещений, вплотную к остеклению.
- Площади подсчитаны по чертежу (в чистоте, за вычетом колонн и вентшахт, без площади проёмов), Площадь тех. ниши 0,88 м² не учтена.
- Мебель показана условно, по исходному плану.
- Контроль масштаба: отрезок 0-5 м на шкале = 100 мм.



УСЛОВНЫЕ ОБОЗНАЧЕНИЯ

- Стена 320 мм
- Колонна 500×500
- Окно, панорамное остекление (витраж)
- Вентшахта
- 4350 Размер по исходному плану

						Квартира: 3 комнаты, лоджия			
						Архитектурные решения			
Изм.	Кол.	Лист	№ док	Подп.	Дата	План квартиры Стены 320 мм	Стадия	Лист	Листов
							Р	1	1
							М 1:50		
							Формат А2		